

A decorative graphic consisting of several overlapping circles of varying sizes, creating a complex, web-like pattern. The circles are light gray and centered behind the text.

CHRISTINE DENESCHUK

Interior Design Portfolio
Graduating September 2026


CONTENTS



3 Restaurant Project



4 Health Care Project

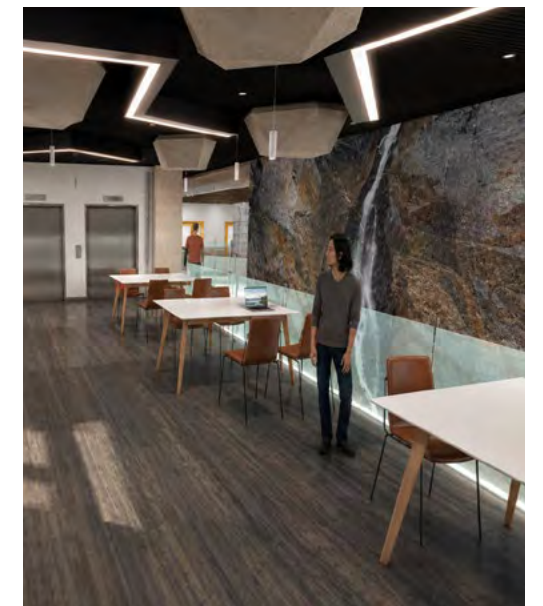

5 Corporate Project

RESTAURANT DESIGN



Restaurant Design Studio, Winter 2025

Location: Kelowna, British Columbia

Area: 2178 s.f.

Mission: To design a hyperlocal, farm to form restaurant with a focus on creating community. Given the floor plan- everything from research, restaurant type, logo design, concept, integration, and design was done to bring the vision of 'renewal' to this project.

Gather is a restaurant focused on creating and engaging community on all levels from design, food sourcing, to patron participation in long table dining.

Notable features of this restaurant design to highlight sustainability and community include:

- Topographical ceiling light of the Okanagan Valley which Kelowna and this restaurant is situated in
- Topography maps carved into host stand millwork and bar
- Second floor mezzanine built for a dedicated aerponic grow towers, and planter boxes
- Long bench community style dining section
- Large plush circular booths to encourage conversation, and privacy at the same time




Community Dining Room: Note the hyper local concept with plant boxes outside. You can see long wooden community bench style seating to encourage conversation and communal style dining. View of the ceiling show the light topography map through the whole restaurant.

Concept: *Renewal*. The renewal dining experience takes you back to the basics to connect with the land and food, and to connect with your neighbours and community. You will see this reflected in the establishment by consuming local foods, in the food grown on site, the decor, and the type of dining offered.


Integration: The decor expresses moving out of darkness into something lighter, lush, and sustainable; moving from isolation into a community. It features a community space to dine as well as a separate area for more private occasions. To help with the hyper local dining- the restaurant will feature food growing towers on the second level.

RESTAURANT DESIGN

Design Development

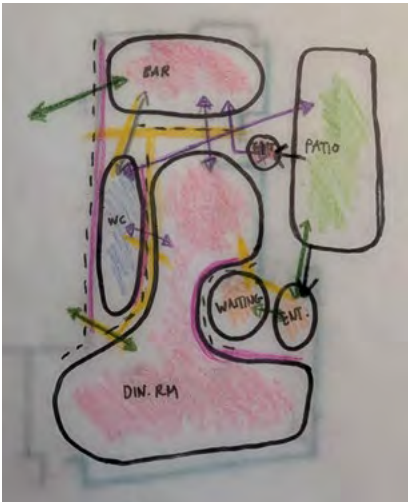


BUBBLE DIAGRAM A AND CHOSEN LAYOUT

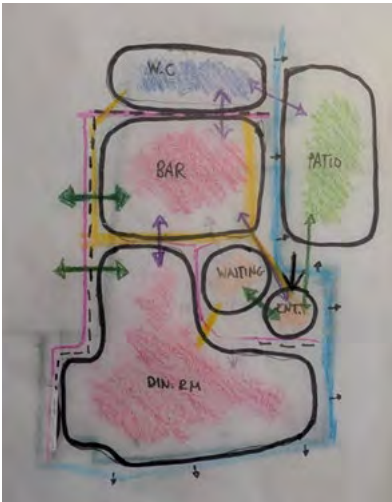

BUBBLE DIAGRAM B




BUBBLE DIAGRAM C

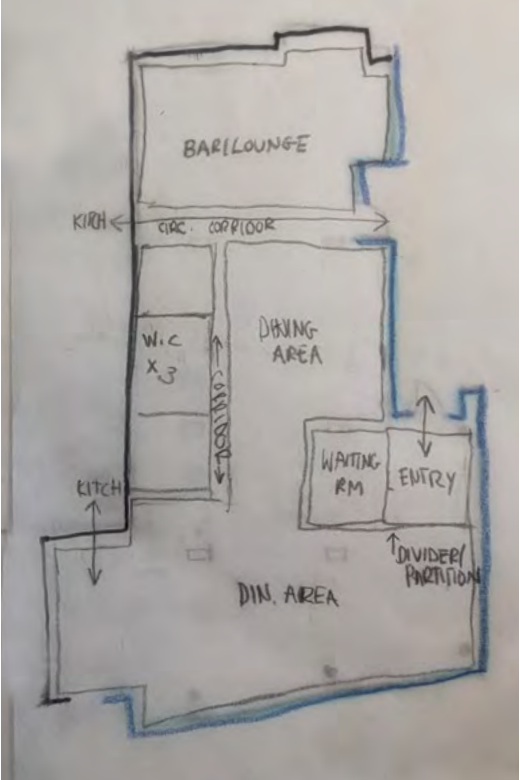

BLOCK DESIGN WITH ESSENTIAL CIRCULATION

BUBBLE DIAGRAM LEGEND

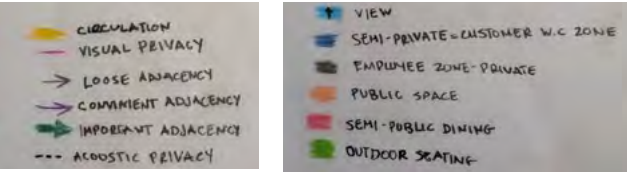

Paint Palette Ecologic Interior Acrylic by Cloverdale.

Venetian Wall 0544, Finish Low Sheen
Location: lounge, waiting area,

Octavius, 0522, Finish Flat.
Location: garden, community area,

Tornado Wind 0584, Finish Low Sheen
Location: bathroom corridor

General Finishes



Midtown Polished Porcelain Tile, in Black by Genrose Stone + Tile.
Location: community dining wall, main corridor to bath-room




Amalfi Green ETC Terrazzo by Eco Terr.
Location: main dining floor



Mod cow carpet tiles by Flor.
Location: main dining floor



Gemma Porcelain Slabs in Notte by Bedrosians Tile & Stone.
Location: community dining wall, all hallways, and bar area.

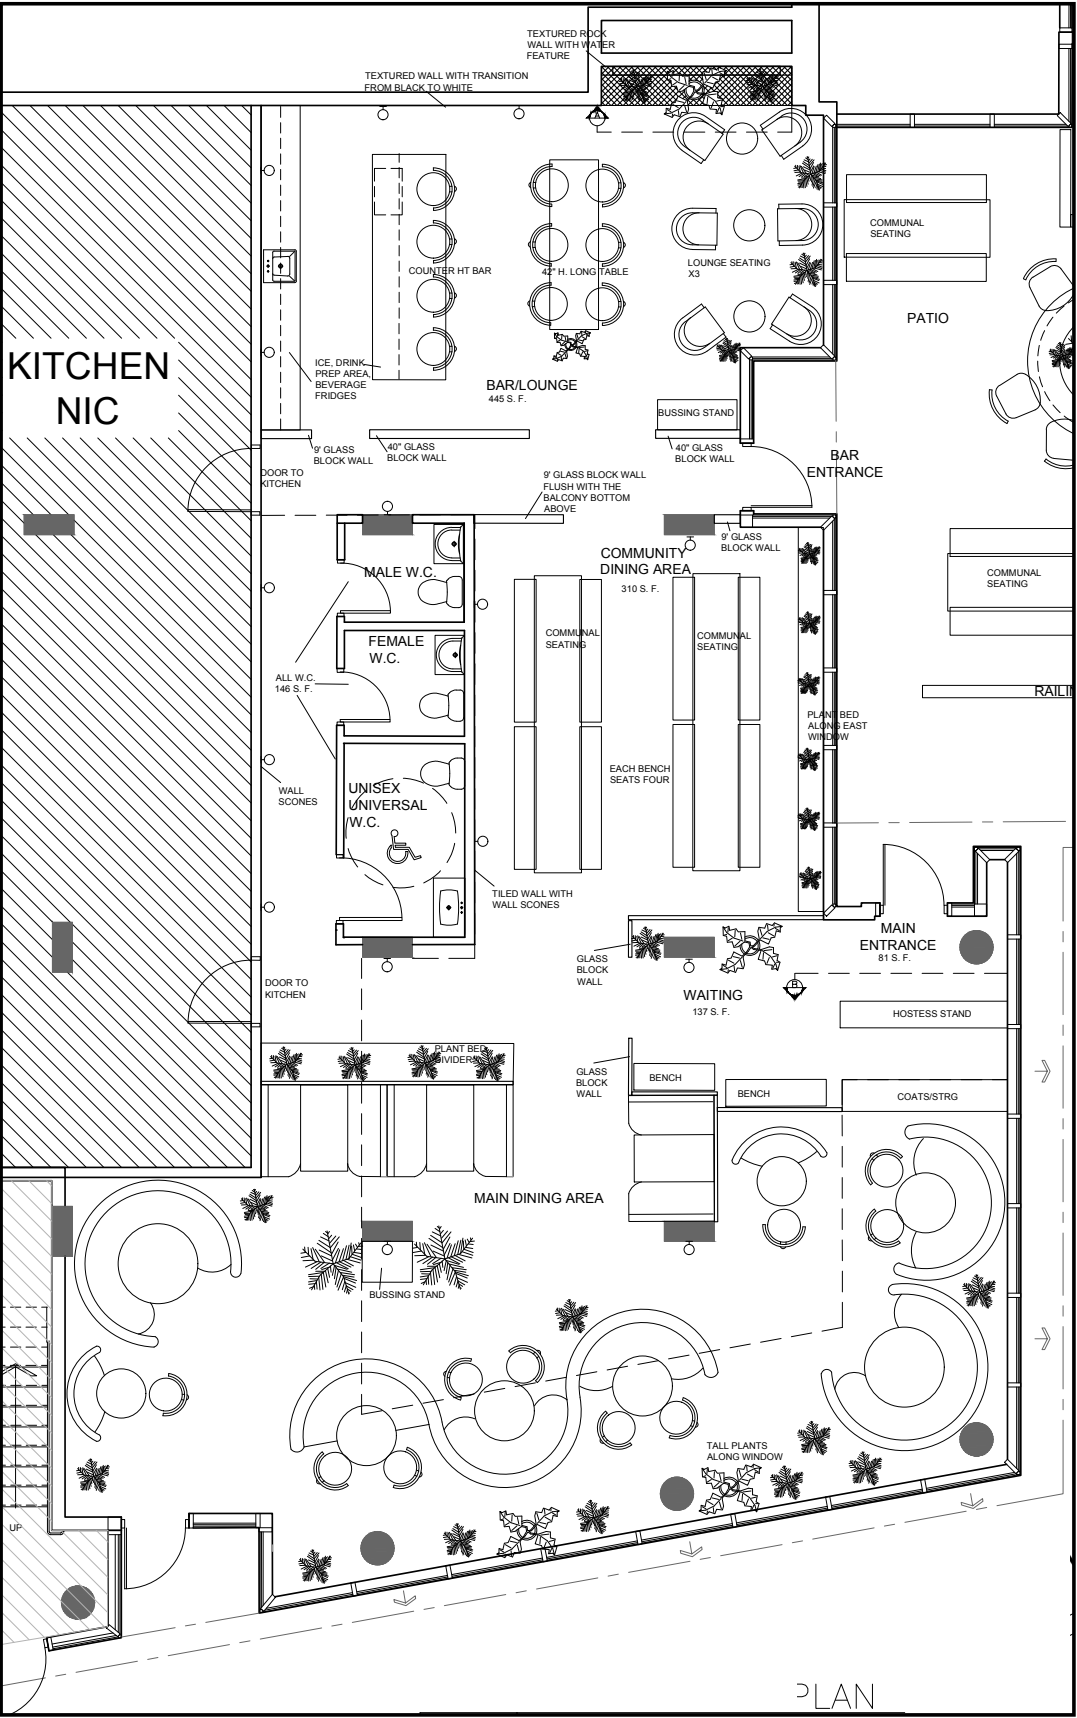

Floor Plan
Scale: 1:50

RESTAURANT DESIGN

Main Dining Furniture and Finishes



Enhanced Dining Experience: (L to R)
Holly curved banquette booths in emerald green velvet by Dynamic Contract Furniture.
2-Coquelicot 23-LA00-S, 2 pendant lamps. Total diameter for two lights 27", by Luminaire Authentik
Ember cafe table by KFI Studios
Venus Chair in three colours: luxe lime, celadon, and rose by Gar Products.



The main dining hall showcases high back private, luxurious velvet booth provide privacy and comfort.

Community Dining Furniture and Fixtures



(Top to Bottom))
Suki portable lamp in Back by Visual Comfort. Integrated LED, 1.35W, 8V, 2700K. Located in all dining areas and lounge.
Waterfall table and bench in Ash Wood by Vermont Farm Tables.
Nubio Ilass block premiere 4" series by Euroverre.
Located in the community dining area, maing dining hall, and lounge.

Bathroom Fixtures and Finishes



High Constrast Bathroom: (L to R)
Spok 60 Anthracite Matte Laminate Sink Vanity by Coycama
Audrey Lane Lively White Porcelain Tile by Trinity Tiles
Kingston wall mount toilet in Black Vitreous China by Kohler
Blue Period 0690, Ecologic Interior Acrylic Finish Flat, GL-1

RESTAURANT DESIGN

Custom Waterfall Wall Design



Elegant Floor to Ceiling Water Feature: (L to R)
Live water and tropical plants
8" Glass Block background by Envor.
Black walnut planter boxes by Armani Fine Woodworking
LED Wall Washer, QCY-XQ-04 by Super Light LED to illuminate the waterfall wall that changes colour.



Bar Lounge Seating: Combination of long tables, and individual occasional tables for a variety of seating beside a beautiful stone waterfall feature.

Lounge Furniture



Diverse Lounge Seating: (L to R)
Pearl lounge two: black metal legs, Wool Chair Fabric by Afra Furniture
Dotti occasional table HPL top in Asian Night and Vinyl Bottom in Lychee
EMBER Table High Pressure Laminate top in Designer White, on a PET Base in Charcoal by KFI Studio
Pearl lounge stool: black metal legs, Wheat and Moss Chair Fabric by Afra Furniture
Wyndam Swivel Counter Stool by Arterior: Mango wood, and iron painted gold

Bar Equipment and Finishes




Not Just Your Regular Bar Equipment: (L to R)
Brushed Champagne Faucet by Dornbracht
Iron/Tones 21" Top Mount Enamel Cast Iron Aspen Green Sink by Kohler
15" Wide Stainless Steel in Sage body and Champagne gold handle- Ice Maker by True
24" W Beverage Fridge: Sage Green Body, with. Rose Gold handle by True
Alison Rose Sfera Mosaic, in Vere Aurora Quartzite, Marble by Artistic Tile


1 Waterfall Elevation
Scale: 1:50

RESTAURANT DESIGN

Ceiling Design

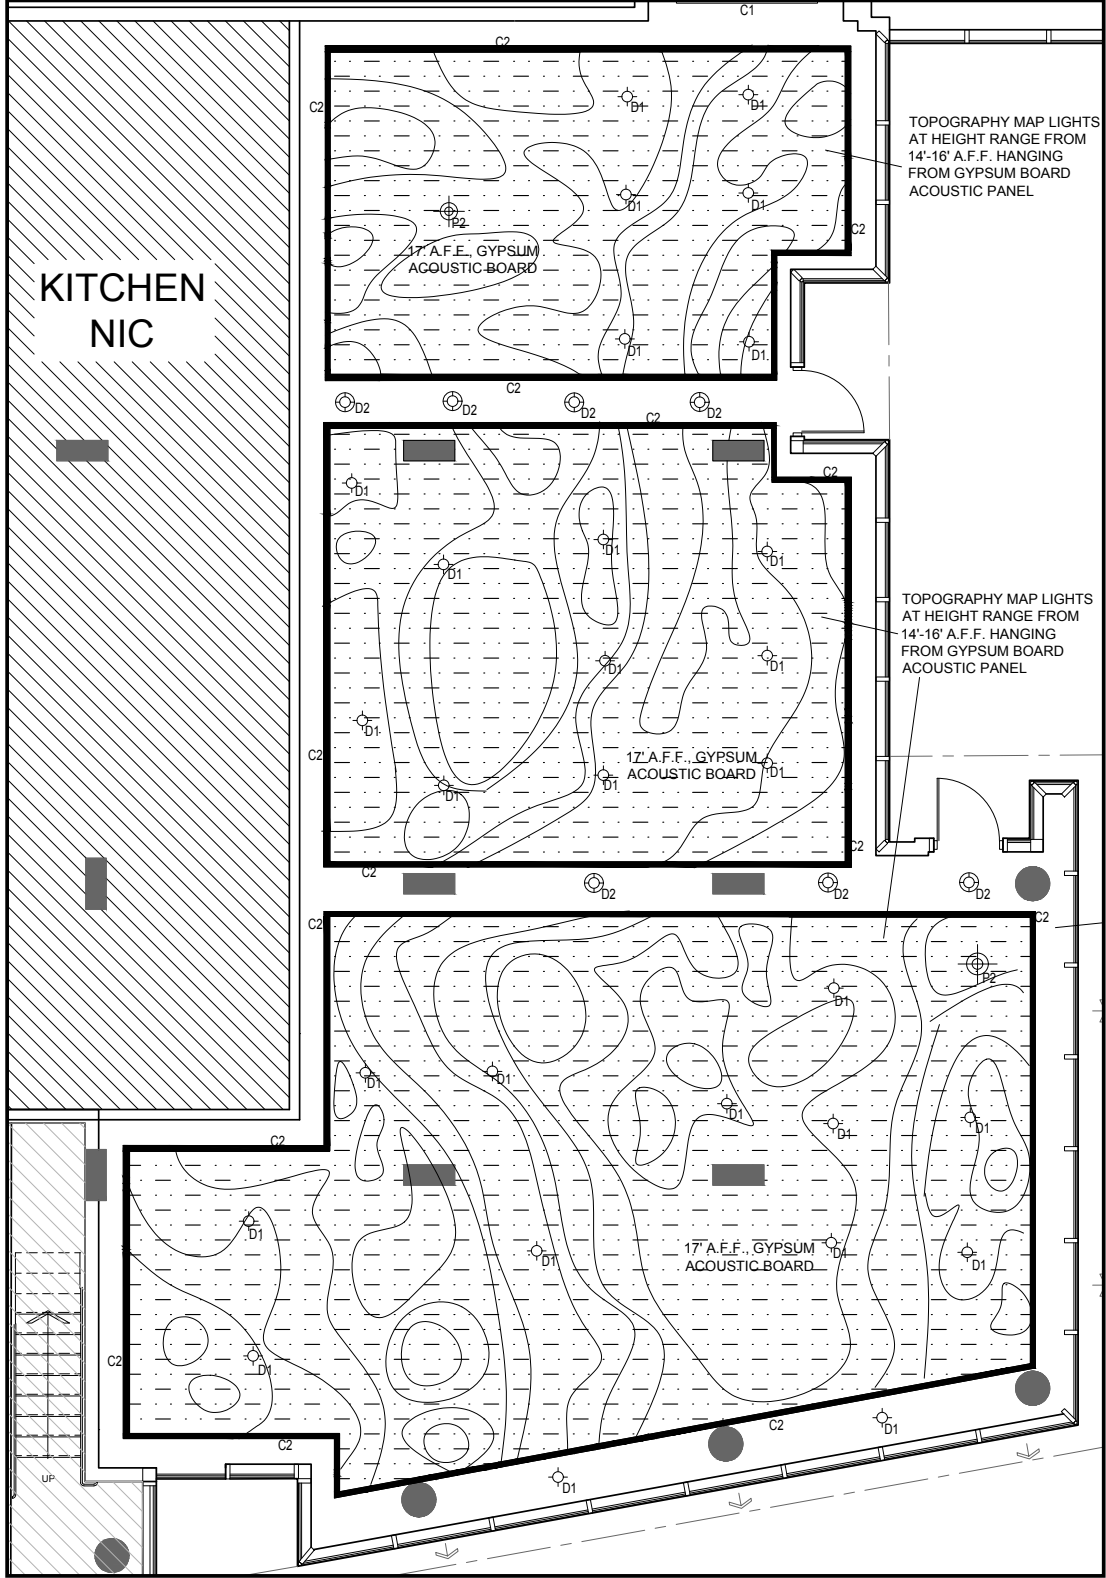

Reflected Ceiling Plan
Scale: 1:50

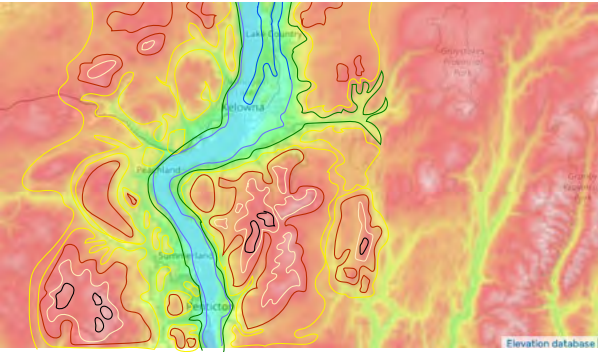

Ambient Custom Light by Acrylicize. Dimmable, Multicoloured, varies in Kelvins, LED
Located in main dining, community dining, lounge.



Balcony with aeroponic grow towers and ceiling light design: The ceiling is a topographical light map of the Okanagan Valley (top left) custom light design by Acrylicize (bottom left). There are three levels of 'height'- hung at 14', 15' 16' from gypsum acoustic board.

Lighting Selection



(L to R) C2-Cove Light, 15255 by Alcon. 25W, Dimmable, 3000K, CRI 90+, 160deg Beam Spread, IP65
Ambient Lighting along all gypsum acoustic board in main dining, community dining, lounge.

D1- 8" Black Housing Vessel, FM-W9100 by Modern Forms. LED, CRI 90, 4000K, ETL, cETL, Wet Location Listed, IP66, Dimmable
Ambient lighting in all areas.

Fluffy, FM- 59922, ceiling mount by Modern Forms. Damp rated, 300k< CRI 9, Dimmable, 31.5W, 2333lm
Located in the bathrooms.



(L) Wall mount Abstract Panels, #2694.98 by Sonneman Lights. 14W, 780lm, 3000K, CRI 90
Located in all hallways, and waiting area.

(R) P2- Ball of Yarn linear pendant by Lights of Scandinavia. 4 x G9, LED bulbs, 3000K, Dimmable.
Located in the lounge.



Loola Boom arm wall light by Open Box. 1 x LED E12 bulb- not included
Located in the community dining area.

Nora Lighting, NS-41B, 4 Inch Stepped Baffle with Ring. 1330lm/ 16.5W, 4000K, CRI 90+
Located in the main dining, community dining, bar.

HEALTH CARE DESIGN



Healthcare Design Studio, Spring 2025

Location: Barrie, Ontario

Area: 376 s.m.

Mission: To design a second floor small health care clinic in an existing medical building. Family physician Dr. Smith and holistic mental health practitioner Dr Jacobson are creating a collaborative practice that blends science of traditional medicine with spiritual and holistic approaches towards mental health.

Notable features of this clinic design to emphasis the seven principles of universal design, and human centered design practices:

- signage for everyone- door names, logo names, instructions will all be written in english, iconography, braille, and have a light colour associated with it.
- ceiling design that leads you around the clinic. Flowing ceiling LED lights that change colour will lead you to the second of the clinic you design- Red wing is for mental health, Blue for physician, and yellow is for auxillary spaces.
- The reception room will have room for multiple chair types: armless chairs, armchairs, bariatric chairs, soft seating, and a special seperate section for those who require added space buffer while waiting.
- Texture-there are fully textured 3D lasered into wood to bring in the calming, grounding element of nature, and give the eye something to rest on to calm the nervous system.
- Light- plays a fundamental element in helping entertain, distract, and guide patients in the clinic from built in LED colour changing in the patient room ceiling,to apply layered lighting to ensure safety and proper working light is in place for everyone.



Welcoming reception area: a circular reception desk with soffit ceiling allows privacy for desk conversations and the ability to for receptionists to monitor the whole area.




Concept: Odyssey. Sometimes navigating healthcare is a journey- or shall we say- an odyssey. This clinic is a multidiciplinary medical clinic that wants to take that long term health journey with you.

Integration: The decor will be light and up beat but draw from nature. There are special sensory features built it to accommodate persons with diverse needs through their life time. Every detail from the ceiling to the texture on the wall was considered to help patient along their odyssey.




HEALTH CARE DESIGN

Design Development

PARTI DIAGRAMS: exploring the feeling of journey in a space

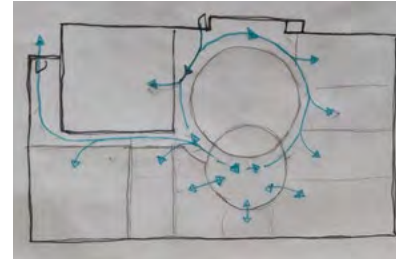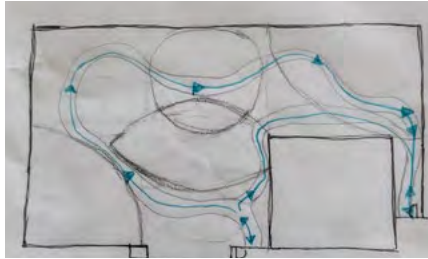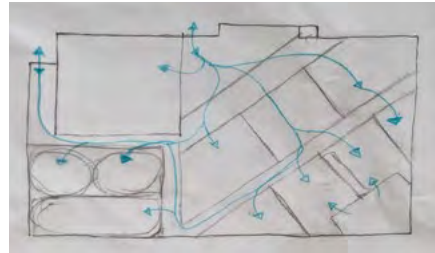


BUBBLE DIAGRAM

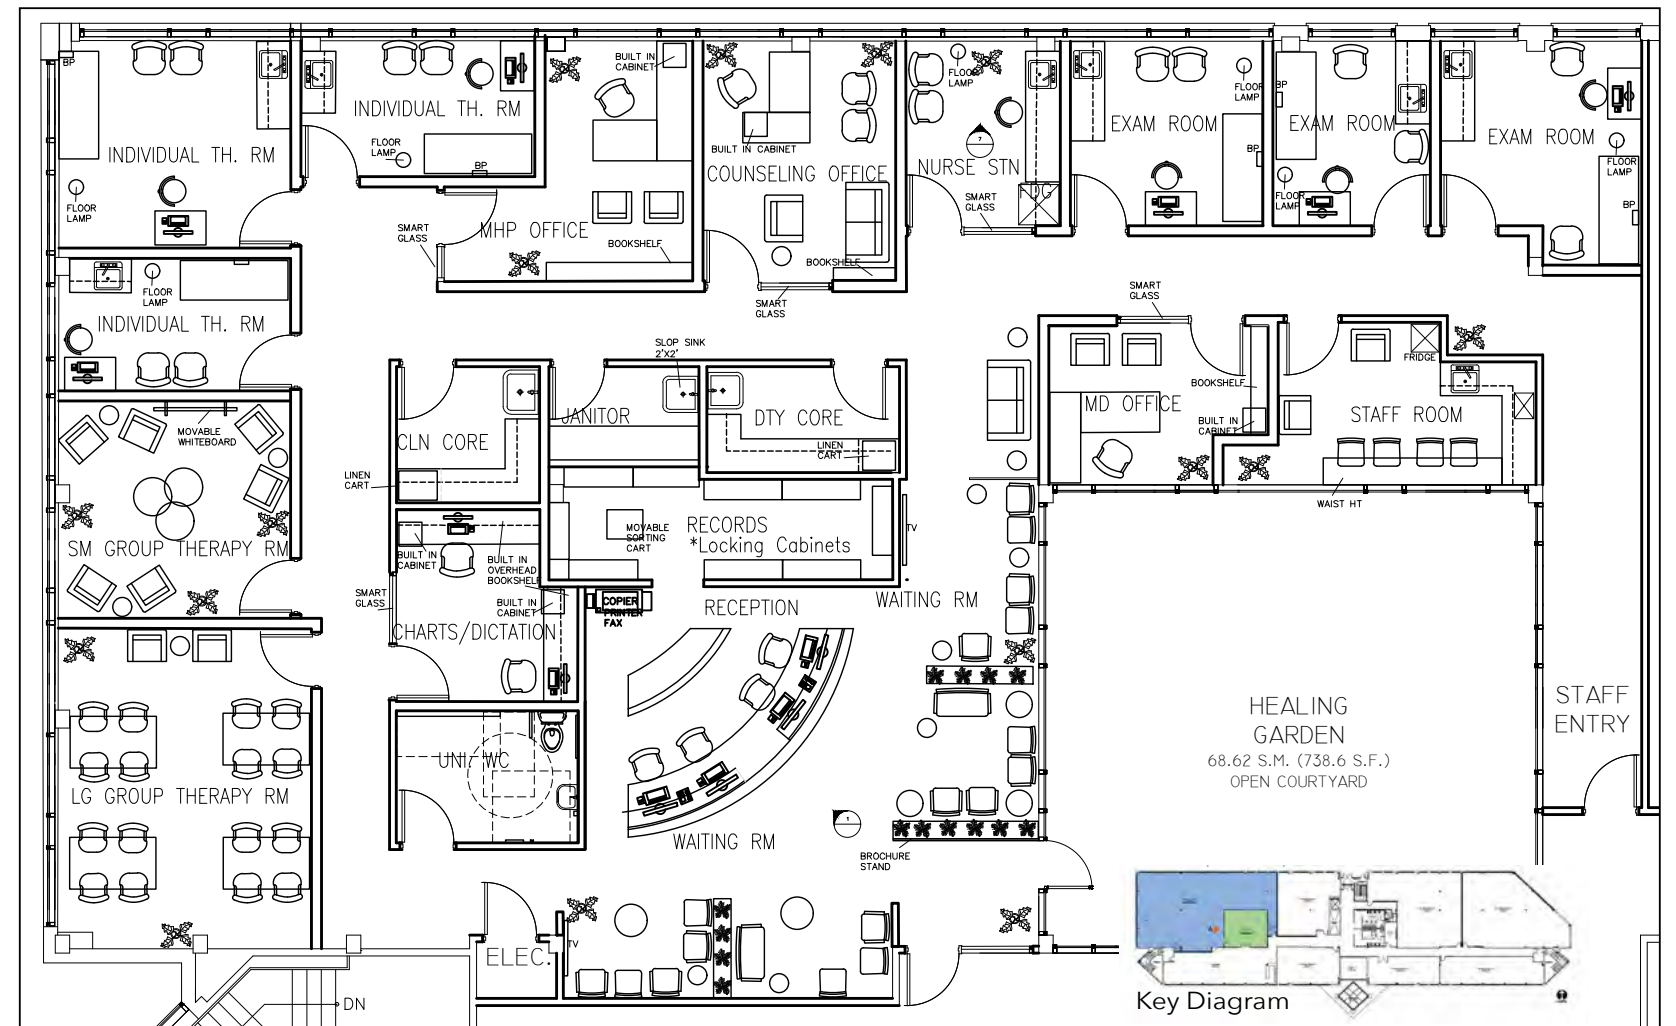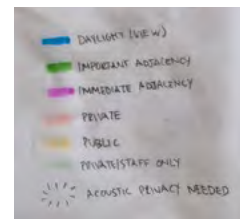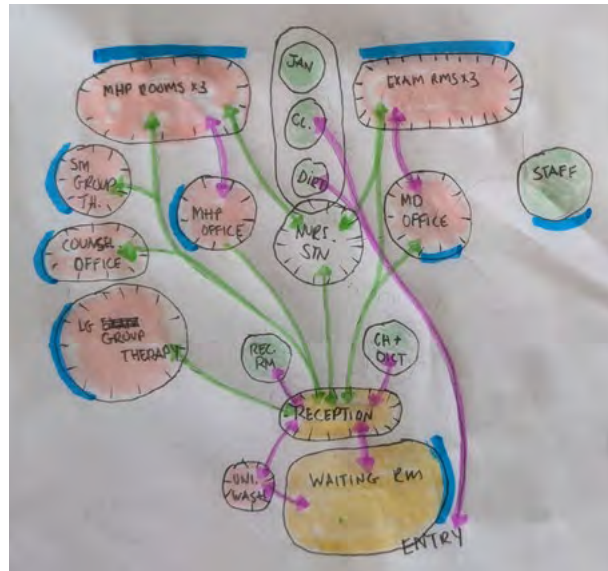

 Floor Plan
Scale: NTS

Concept Development

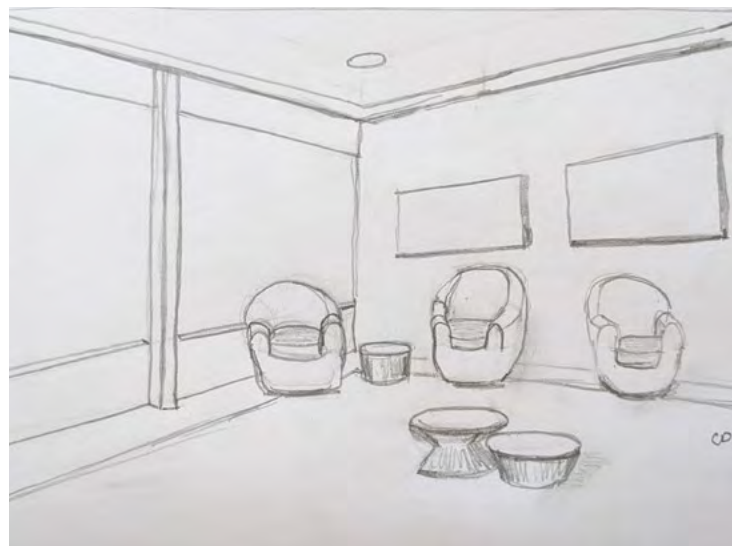

INITIAL DRAWING EXPLORATION: Group Therapy Room

Paint Palette

Paint by Sherwin Williams



Accent wall paint- Venetian Wall 0544
Location: lounge, waiting area

General wall paint- SW 9505 Frost Bite
Eggshell.
Location: all areas

General Finishes



Verme Decorative wood wall with Logo in natural baltic
birch plywood by Soelberg
Location: Staff room, reception area

Hanex Acrylic BL-302 Linen White Laminate.
For reception desk, all counter tops.



Raw Chestnut Woodgrain Laminate Soft grain Finish.
For reception desk, hallways, plant box, and chair legs.

Flooring



Rubber Tile in Deep Navy by Roppe
Location: hallways, staff room, treatment rooms, nursing rooms, therapy rooms, offices, reception.



Rubber Tile in Snow by Roppe
Location: hallways, staff room, treatment rooms, nursing rooms, therapy rooms, offices, reception.



Society AV Carpet, Aged Bronze Encore Hospitality Carpet.
Location: therapy rooms, reception, offices

HEALTH CARE DESIGN

Custom Reception Desk Design

This custom reception desk design is full accessible for patients and contains all the ideal occupational health and safety dimensions for the receptionists.




Logo on natural baltic birch
lazered plywood by Soelbergi

Location: Staff room, reception area,
hallways




Raw Chestnut Woodgrain
Laminate Softgrain Finish
For reception desk, plant box, and chair
legs

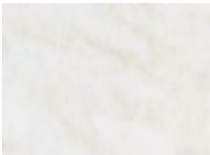

Hanex Acrylic BL-302 Linen
White Laminate
For reception desk, all counter tops



Accent wall paint- Venetian
Wall 0544, Ecologic Interior
Arcylic Finish Low Sheen,
GL-4 by Sherwin Williams
Location: staff lounge, waiting area

 


General Wall paint- SW 9505
Frost Bite Eggshell Paint by
Sherwin Williams
Location: all areas




Reception area: incorperates plants and light woods to help soothe the nervous system, and a wave like ceiling lighting system to help direct and entertain patients.

Reception Area Furniture and Finishes

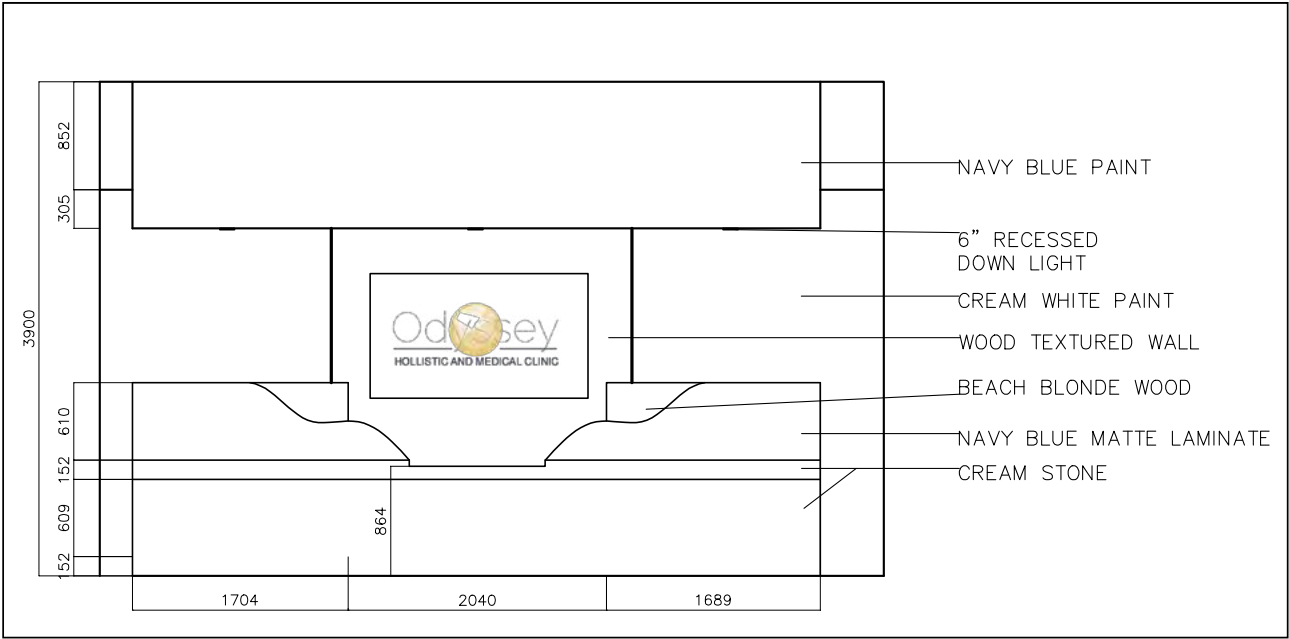


1 Reception Desk Elevation
Scale: 1:50

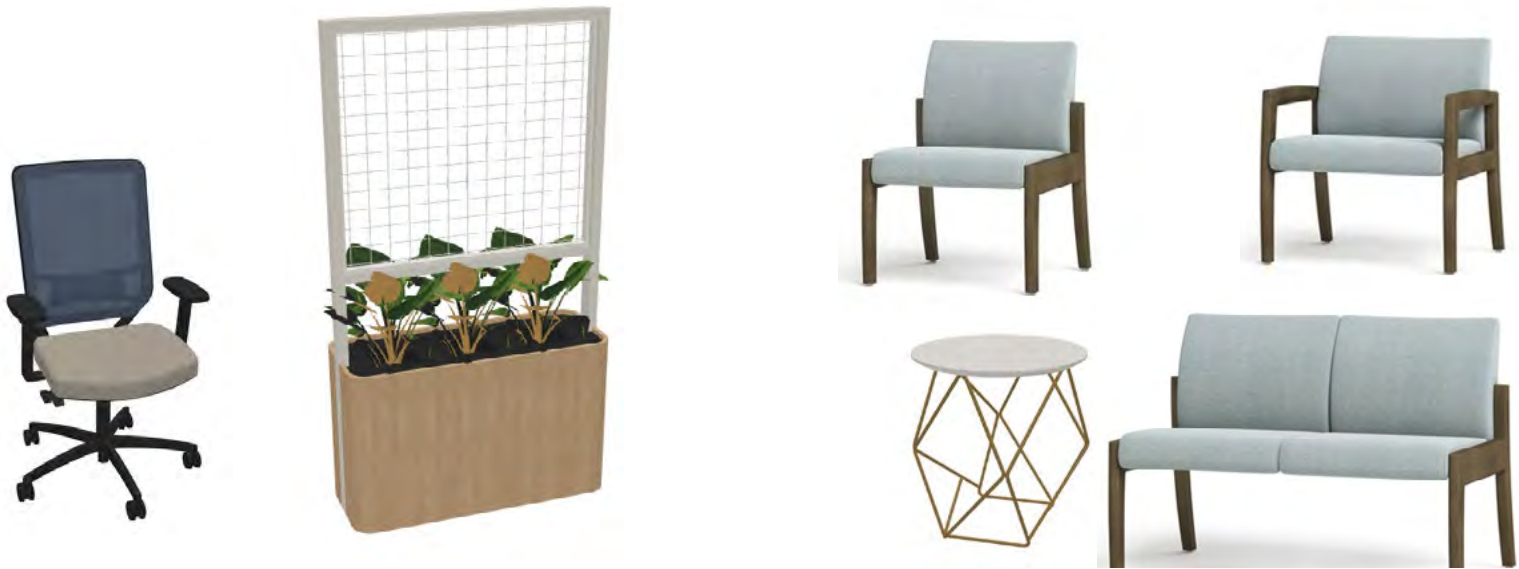

Grounding Waiting area: (L to R)
Genus High Back-Mesh back in blue by OFS.
Hydra Planter by OFS.
Carolina Task Chairs in Lynx in Arbor Obrina and CF Stinson- Gabby Ore by OFS. Three differ-
ent styles for a variety of seating: armless, bariatric chair, and multiseating style.
Maive 18" and 30" Coffee Table in gold and white top by OFS

HEALTH CARE DESIGN

Treatment Room Furniture and Finishes: (L to R)

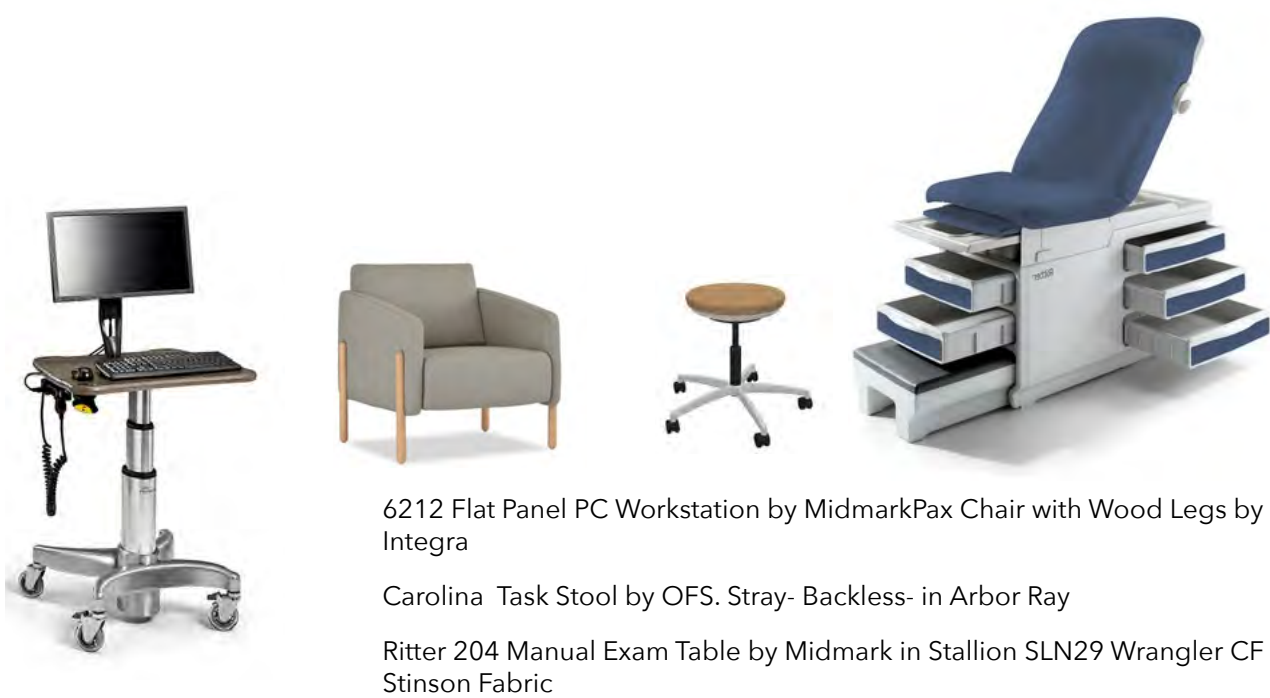

6212 Flat Panel PC Workstation by MidmarkPax Chair with Wood Legs by Integra
Carolina Task Stool by OFS. Stray- Backless- in Arbor Ray
Ritter 204 Manual Exam Table by Midmark in Stallion SLN29 Wrangler CF Stinson Fabric



ColourFLEX Brittany Style by Cabinet Pro. Expertly matching Sherwin Williams paint
Lower Cabinet Colour: 377 Butterscotch. Satin
Upper Cabinet Colour: SW7566 West Highlands White



Treatment Rooms: Each treatment room will have be finished with cheerful finishes and a decorative ceiling lined with LED strip lights that change colour in Acousticbuilt Seamless Acoustic Ceilling by Armstrong.

Small, Large Therapy Room Furniture and Finishes



(L to R) Tenor Chair by Steelcase Learning.
Applause Table by OFS.
Maive 30" Coffee Table by OFS.
Embrace Chair CHE005 by Carl Hansen & Son in blue and tan. Also located in the Staff Room, and Office Guest Chairs.



HEALTH CARE DESIGN

Lighting Selection



Catalonia, FM-60217-AB, Aged Brass Ceiling Mount light by Modern Forms
Located in charts, clean/dry core, janitors room



Lea, LA04G-LD x3 by A Emotional Light.
Decorative light in reception and small therapy room.



Ophelia, WS-72210-AB, Aged Brass Wall mount by Modern Forms
General Ambient in hallways, reception area, therapy rooms



Anel, Ref. AN05 by A Emotional Light.
Decorative and ambient Located in large therapy room.




Pili medium, PL04 by A Emotional Light.
Decorative light in offices



L1- Bluetooth White Recess downlight, RGL-6B-9W-BT (6'') by National Specialty Lighting.
Ambient light in every room.



Dixon Cone Pendant, Verde Lichen Finish by Pax Lighting
Decorative light in the bathroom

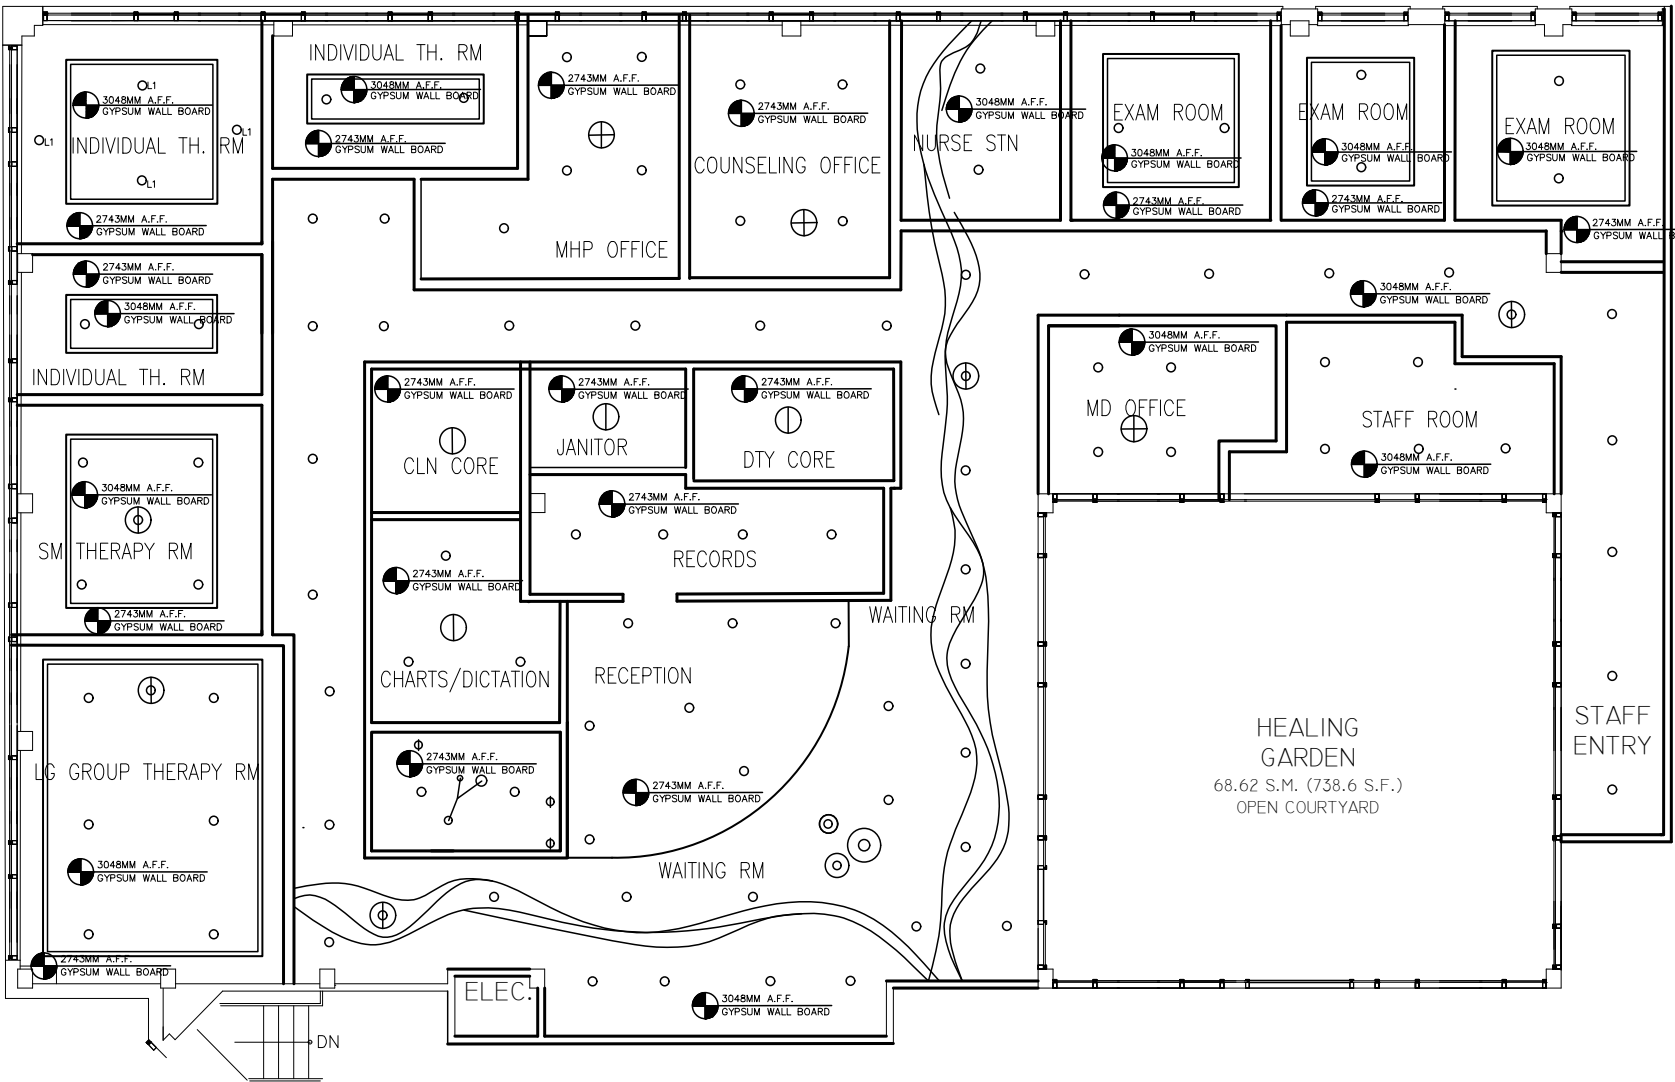

Reflected Ceiling Plan
Scale: NTS

Office Furniture



Haven Office Furniture System: Bookshelf, desk with return, cabinet. by Herman Miller in Clear on Ash Wood Veneer.

Bathroom Equipment and Finishes (L to R)



Oblo Curve touchless soap and faucet by Kohler.
Kingston Ultra White Porcelain Sink by Kohler.
Soho Low Flush, AutoFlush Commercial Toilet by Kohler.
Flatiron White Matte by Angela Harris porcelain tile, slip resistant, chemical resistant, low VOC by Tilebar.
Motor City Circles Vanilla Onyx backsplash tile in nursing station, around sink in bathroom, staff room by Artistic Tile.

CORPORATE DESIGN



Corporate Workspace Design Studio, Summer 2025

Location: Toronto, Ontario

Area: 2 Floors- 17,508 s. f.

Mission: To design a two floor office space for a software company. The design goal for this project is to create an innovative work environment that stimulates interaction and enhances opportunities for collaboration.

Notable features of this workspace design to emphasize the innovative work environments and human centered design:

- casual gathering spaces to promote social engagement on both levels
- biophilic design through the space including a real rock wall feature in the lobby
- sit to stand work desks at all work stations
- acoustic control through textured wall and ceiling finishes.
- modular furniture in cubicle environments to adjust to more or less employees
- open central staircase to encourage open, visible spaces and a health, quick alternative to the elevator.
- sustainable material choices
- ADA and code compliant circulation and work spaces
- Variety of seating on both levels
- Integrated LED layered lighting in all rooms




Custom reception desk design and reception space. This custom reception desk is the first thing you see as you enter from the elevator. It is fully accessible and incorporates universal design. It is high lighted by pendant ceiling lights to the back drop of a floor to ceiling rock wall formation.

Concept: Canadian Shield. Wanting to reflect Ontario in its new headquarters while honoring the values the company, the concept of "Canadian Shield" was a natural fit. The Canadian Shield is an ancient rock formation from Precambrian times. Unity and the Canadian Shield embody respect for the local environment, solid foundation, timeless existence, and nature. Within the Canadian Shield it holds a bio diverse landscape with holds space for all- thick and thin, chaos and calm, light and dark, rigid and flexible. It represents a stable, timeless, organic, grounded platform for focused innovation and collective creativity. It is defined by rock, forest, and freshwater.

Integration: This theme will show up in beautiful bold natural materials and textures, organic forms, clean lines, with diverse yet harmonious furnishings, and lighting by prioritizing diffused natural light to as many office spaces as possible.

CORPORATE DESIGN

Design Development

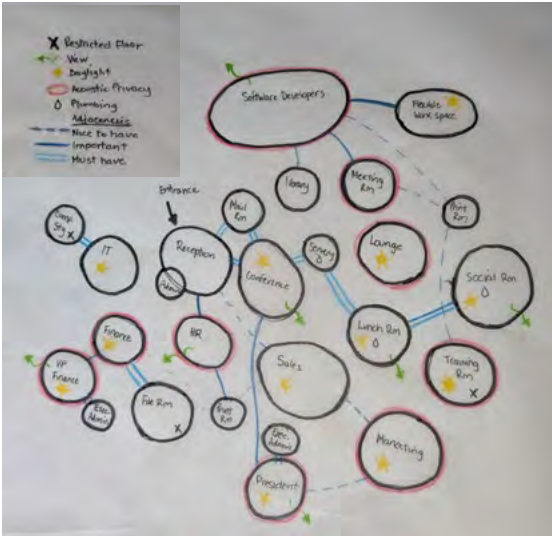

BUBBLE DIAGRAM B



BLOCK DESIGN FROM DIAGRAM B
1st Floor




BLOCK DESIGN FROM DIAGRAM B
2nd Floor

Paint Palette

Benjamin Moore Eco-spec Interior Paint in Eggshell:



All hallways, and indicated accent wall
colour Hale Navy HC-154

 

General wall paint colour Calm OC-22



*This symbol indicates that the products have been sustainably sourced and have reduced environmental impact in a variety of ways.

Main Floor Finishes



Milliken Luxury Vinyl Tile in WIL98
Walnut 6" x 48"
Location: lunchroom, meeting room, library



Milliken Frequency Carpet in Charcoal
Location: social room, meeting room, conference room, executive rooms, lounge, finance



Liquid Elements- Custom Matte Finish Resin Floor
Located in the hallways, library, printer rooms, mail room, file room, reception, IT department, executive administrator area



First Floor Plan
Scale: 1/8" = 1'0"

CORPORATE DESIGN




Second Floor Plan
 Scale: 1/8" = 1'0"

Reception Area Furniture and Finishes



Custom Rock wall Feature spanning 2 floors
 Location: reception and flexspace



Cosima Modular Sofa- Green
 Location: social room, reception
 Steelcase Sebastopol Tables
 Location: lounge, social room and reception area

Software Developer Furniture (L to R)



Frank Lloyd Wright Galesburg Lounge Chair
 Tronco Table for meeting space: 32.67" W x 32.67" D
 Haworth Fern Task Chair- in Moonflower and Carbon with black trim. Also located in all offices, reception, executive administrators, in various colours.
 Steelcase Currency Enhanced Lateral Filing Cabinet and Credenza: 18 7/8 "D x 72"W
 Steelcase Currency Overhead bins 36"-75"W x 16" D x 15"H
 Currency Slim Leg Height-Adjustable Desk: 30" D x 60" W



(Above) Steelcase Answer Panel dividers in light grey and charcoal with:
 a) 1' clear glass top. 72" High, or,
 b) top half portion of the panel will have a whiteboard section.

CORPORATE DESIGN

A1 Cross Section Elevation




Lounge Chaise




Daal's Byron Pillow
Edge One Seat
Chaise- in Moss Green
Velvet and Beige
Location Lounge

Conference Room (L to R)

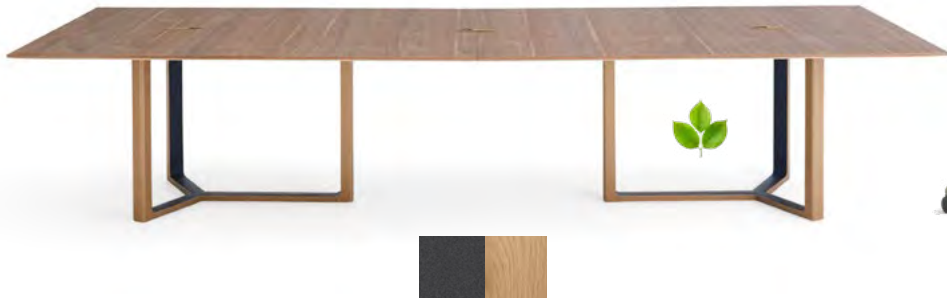

Steelcase Verlay Conference Table for
16- planed oak top, matte charcoal
legs
Location conference room

Steelcase Marien152 Conference Chair
Location conference room
Seat Back in Leather Chamoise, Base in Forest
Green, Metal is black

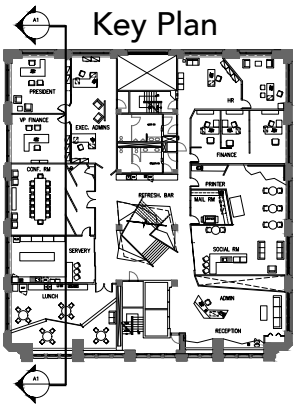


Fuse MPS acoustic baffles with built in lights.
Location: lunch room and servery (1st floor far left two rooms)


Executive Finishes



Furniture Bases and Metal:
Jet Black

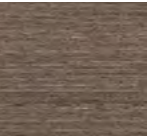

Veneer finish: Dove Grey
by Techwood veneer

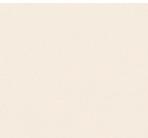

General Fabric: Light
beige

Executive Flooring



Carpet Tile: Milliken Clean
Break Modular in GOC133
Observant



Carpet Tile: Milliken Clean
Break Modular GOC251
Effective

Executive Furniture: (L to R)




Knoll Reff 72" credenza and wall-hung overhead bins
with Reff 72"H x 36"W lateral freestanding cabinets
Knoll Reff height adjustable peninsula desk

78 "W x 36" D x 26.5-42.25"H
Knoll Pilot high back chairs with arms in Classic Bou-
cle- Pearl upholstery colour



CORPORATE DESIGN

Lighting and Ceiling Details

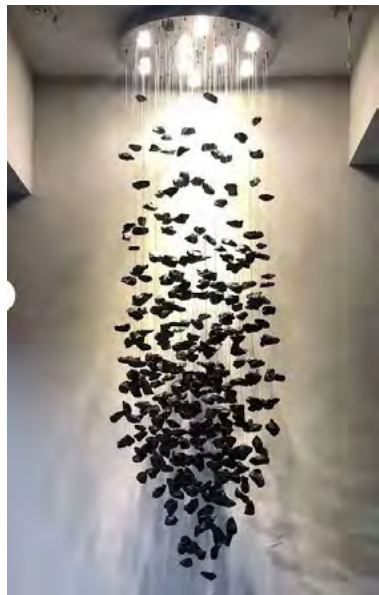


L6(L8)-Zest by Modern Chandeliers Staircase Chandelier- Black Stones
Located: central staircase, reception




L4- 4" Baffled Square LED Can Light, Model 14009-4
Located: conference room, executive rooms, lounge, meeting room, refresh bars, training room, finance department, HR department, software developer room, lunch room

TAG/SYMBOL DESCRIPTION	
	2-Inch LED 3D Linear Lighting System-VAR. SIZES
	2-Inch Square LED Linear Pendant Light- VAR. SIZES
	2.5-Inch Y-Shaped LED Pendant Light
	4-Inch Baffled Square LED Can Light
	4.5-Inch Opal Tall Drop Lens LED Cylinder Pendant with indirect Light
	ZEST MODERN CHANDELIER
	2-Inch Ceiling-to-Wall Recessed LED Strip Light
	ZEST MODERN CHANDELIER-CUSTOM PATH
	Planar 3000K Adjustable Horizontal Pendant LED Light 42"
	Planar 3000K Adjustable Small Pendant LED Light
	SQ LINEAR LED PENDANT LIGHT IN MPS ACOUSTIC FUSE CEILING

TAG/SYMBOL DESCRIPTION	
	ACOUSTIC CLOUD
	FUSE BAFFLE IN GREY
	CREEP CEILING AND WALL FAUX BEAMS

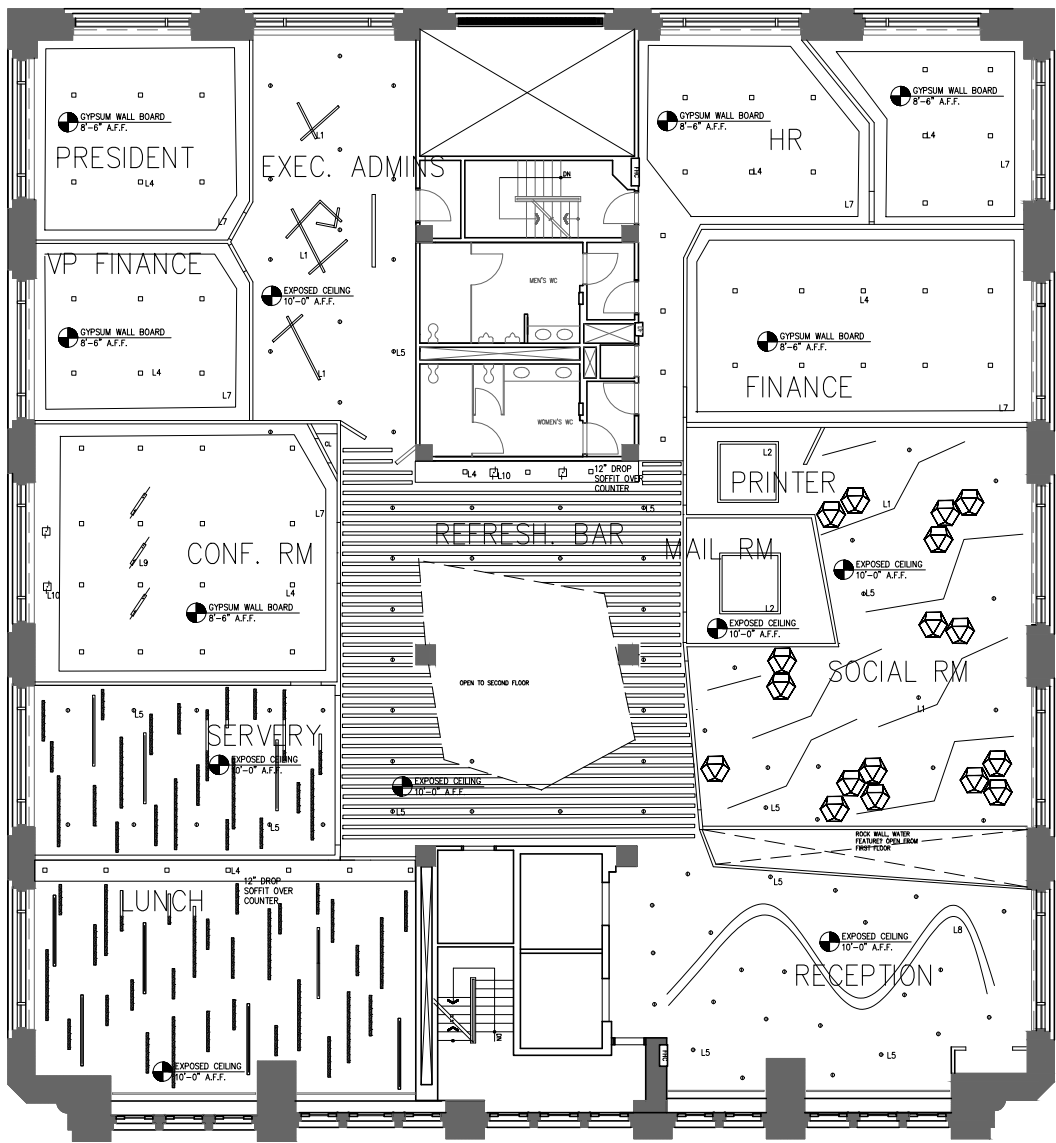

First Floor Reflected Ceiling Plan
Scale: 1/8" - 1'0"

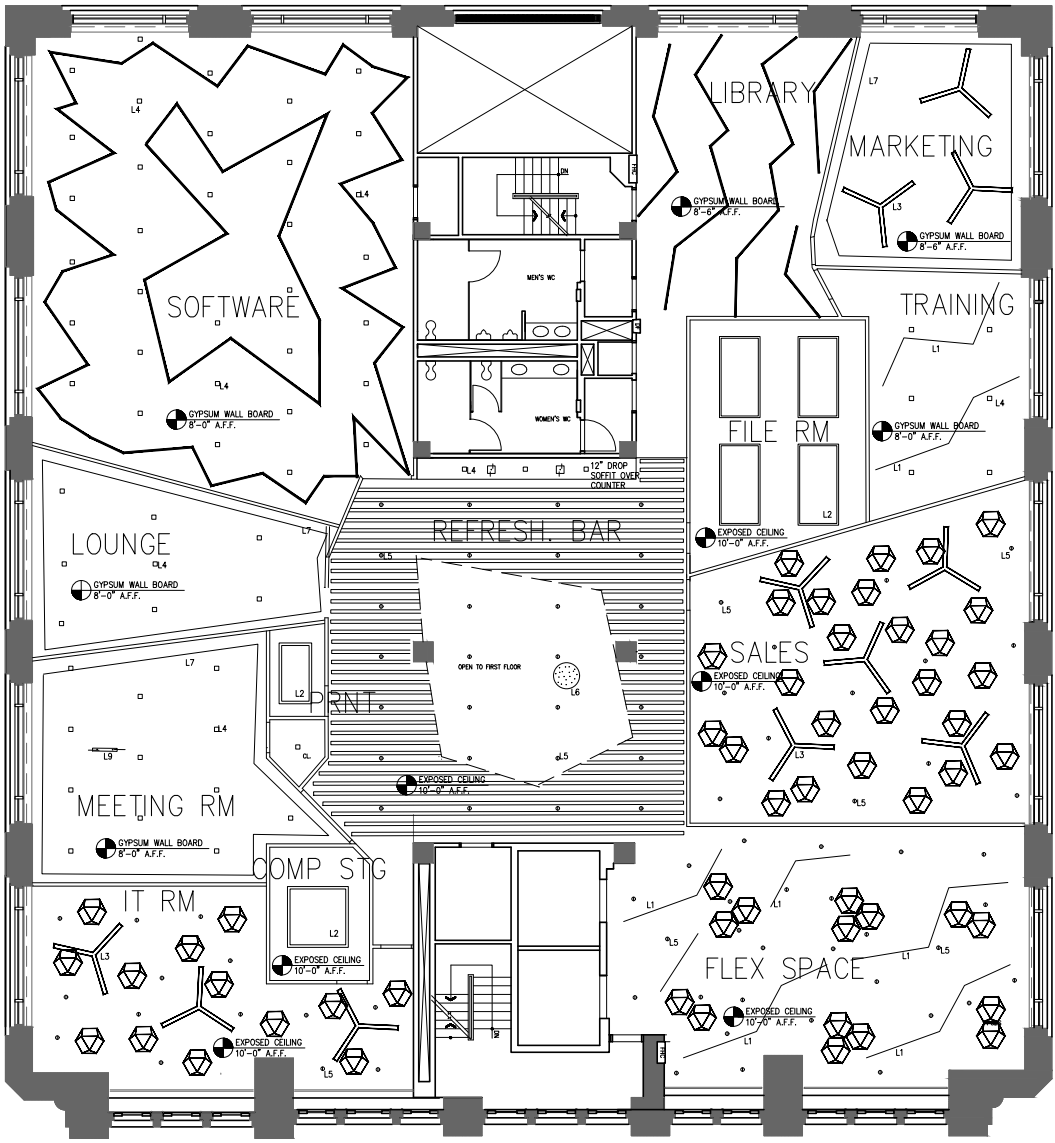

Second Floor Reflected Ceiling Plan
Scale: 1/8" - 1'0"




L7- 2" Ceiling-to-Wall Recessed LED Strip Light
Location: conference room, executive rooms, lounge, meeting room, library, training room, finance, HR, software, lunch room, refresh bars, training room.



L1.1 Chaos Sconce
Location: meeting room, library, lunch room, servery, lounge



L2- 2' Square LED Linear Pendant
Location: computer storage, file room, ,ail room, printer rooms

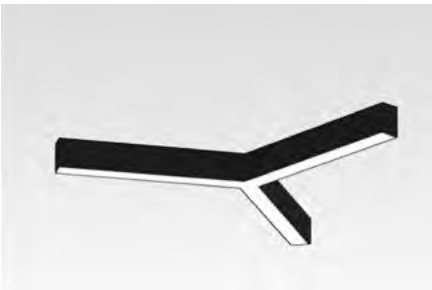

L3- 2.5' Y-Shaped LED Pendant
Location: marketing, IT department, sales department



L10- Planar 3000K Adjustable Small Pendant LED Light- in Dark smoke
Location: meeting room, conference room



L9- Planar 3000K Adjustable Horizontal Pendant LED Light- in Dark smoke
Location: Meeting room, and conference room

CORPORATE DESIGN

Common Hallway Ceiling and Lighting




L5-4.5" Opal Tall Drop Lens LED Alcon Cylinder Pendant Light
Located: Executive administrator area, main hallway, flex space, social room, servery, reception, IT department

(R) MPS Creep Faux wood Acoustic Beams in Major Hallway and center space.




Refresh Bar Furniture and Finishes

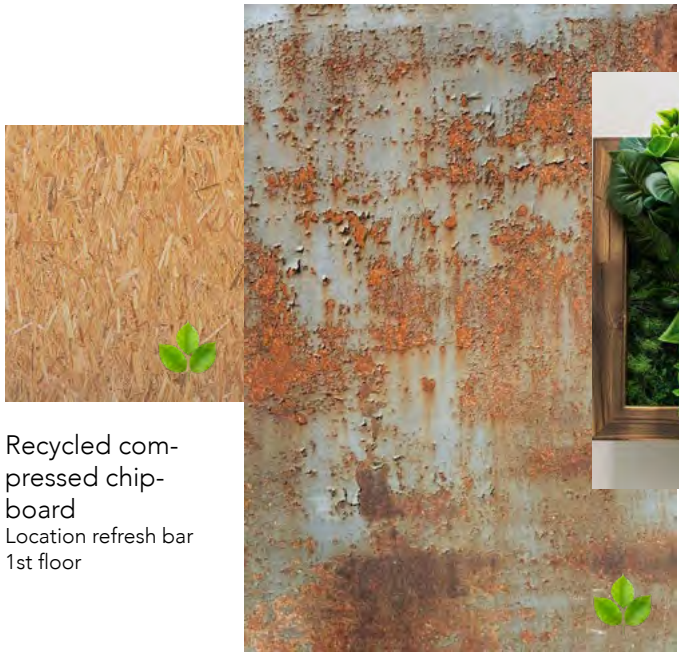


Recycled compressed chipboard
Location refresh bar 1st floor

Recycled custom metal featured wall
Location: refresh bars- 1st and 2nd Floor, Social Room

Vertical plant wall
Location refresh bars- 1st and 2nd Floor, Social Room

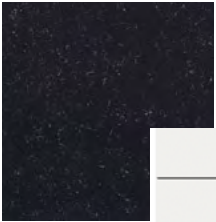

Daltille Quartz counter top in nightfall
Location: refresh bars, lunch room, servery, reception, social room

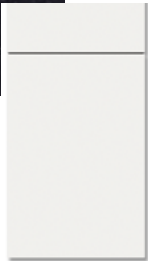

Nieu's Scandia flat panel cabinet design in Snowbound SW7004 (Whimsical White)
Location: refresh bars, lunch room, servery, reception, social room



(L) m.a.d. Furniture Sling Chair High Stool
Location 2nd Floor Refresh Bar Tables



(R) 2" Emeco Bar Height Table- black base and white laminate top
Location 2nd Floor Refresh Bar Tables

(R) Indoor Bean Bag (XL) - Quilted Kyoto collection in Speed Blue and Power Grey
Location Refresh Bar 1st Floor




CORPORATE DESIGN

Marketing Department Furnishings



Finishes:
Base/Metal Paint: Merle 7360
Laminate top: Aged Ash 8844-58
Cushion top: Stencil Honeydew P468

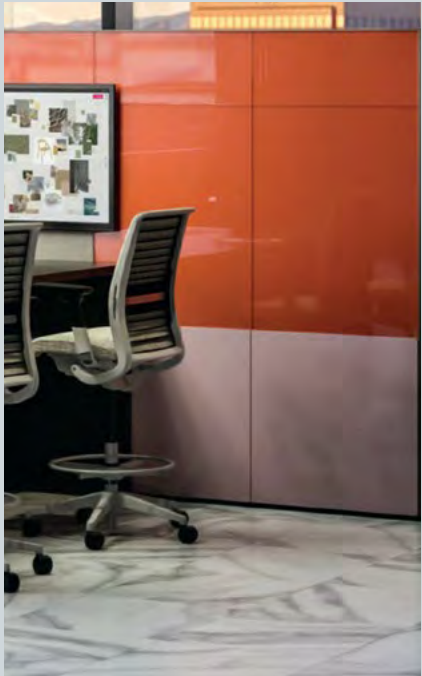

(L to R) Steelcase TS series pedestal with seat 2 drawer cabinet- 36" W
Steelcase Migration SE adjustable desk- 35"D x 70"W
Steelcase TS series overhead bin- 36" W
Steelcase TS series lateral filing cabinet stationary, 2 File drawers- 36" W
Haworth Fern task chair- in coal and balsam with black trim. Also located in all offices, reception, executive administrators, in various colours.
Steelcase Answer panels:
a) between desks- 54" H panel with whiteboard top,
b) at the door- 66" H panel with whiteboard top. In Light grey and white.



Flexspace Furniture and Finishes

Flex space. Located on the second floor, this space is a flexible space that can be used for unofficial gatherings, work breakout sessions, quiet lunches, and more. It connects to the reception below with an open faced rock wall, but also has acoustic pods and felted acoustic pebble clouds to mitigate the noise.



L1- 2" Regressed LED 3D Linear Lighting System
Location: Social Room, flex space, executive administrator area

Kirei Convex Clouds in Pebble
Location: Flex space, Sale department, IT department, Social room

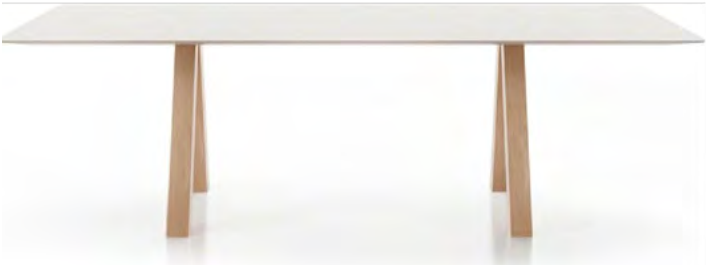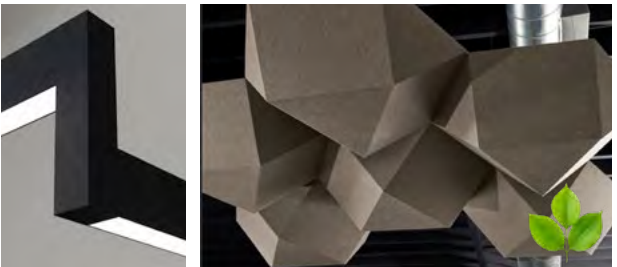

m.a.d. Furniture Sling Chair. seat colours: Leather in Rust, Forest Green.
Location Lunch room, flex room, social room, training room, meeting room library

Trestle Table by Viccarbe Top White Laminate with wood legs- 29" H x 36"D x 72"L
Location Flexspace

Herman Miller Bay Work Pod Pro- Grey
Location Flexspace

DESIGN PHILOSOPHY

Communication. Integrity. Creativity.
Professional. Unique. Personalized.
Local. **Illuminating**. Sustainable. Grass
Roots. Artisan. Out of the box.
Passion.

I value sustainability, creativity, and communication. I am able to incorporate these values in many ways with design to create harmonious, curated, well lit spaces for every client. As we move along the design journey- I treat lighting as not just a necessary functional thing but a beautiful thing taking a space to new levels.



Thank you. Look forward to hearing
from you.

Christine Deneschuk

deneschukc@gmail.com
+1-403-966-6002